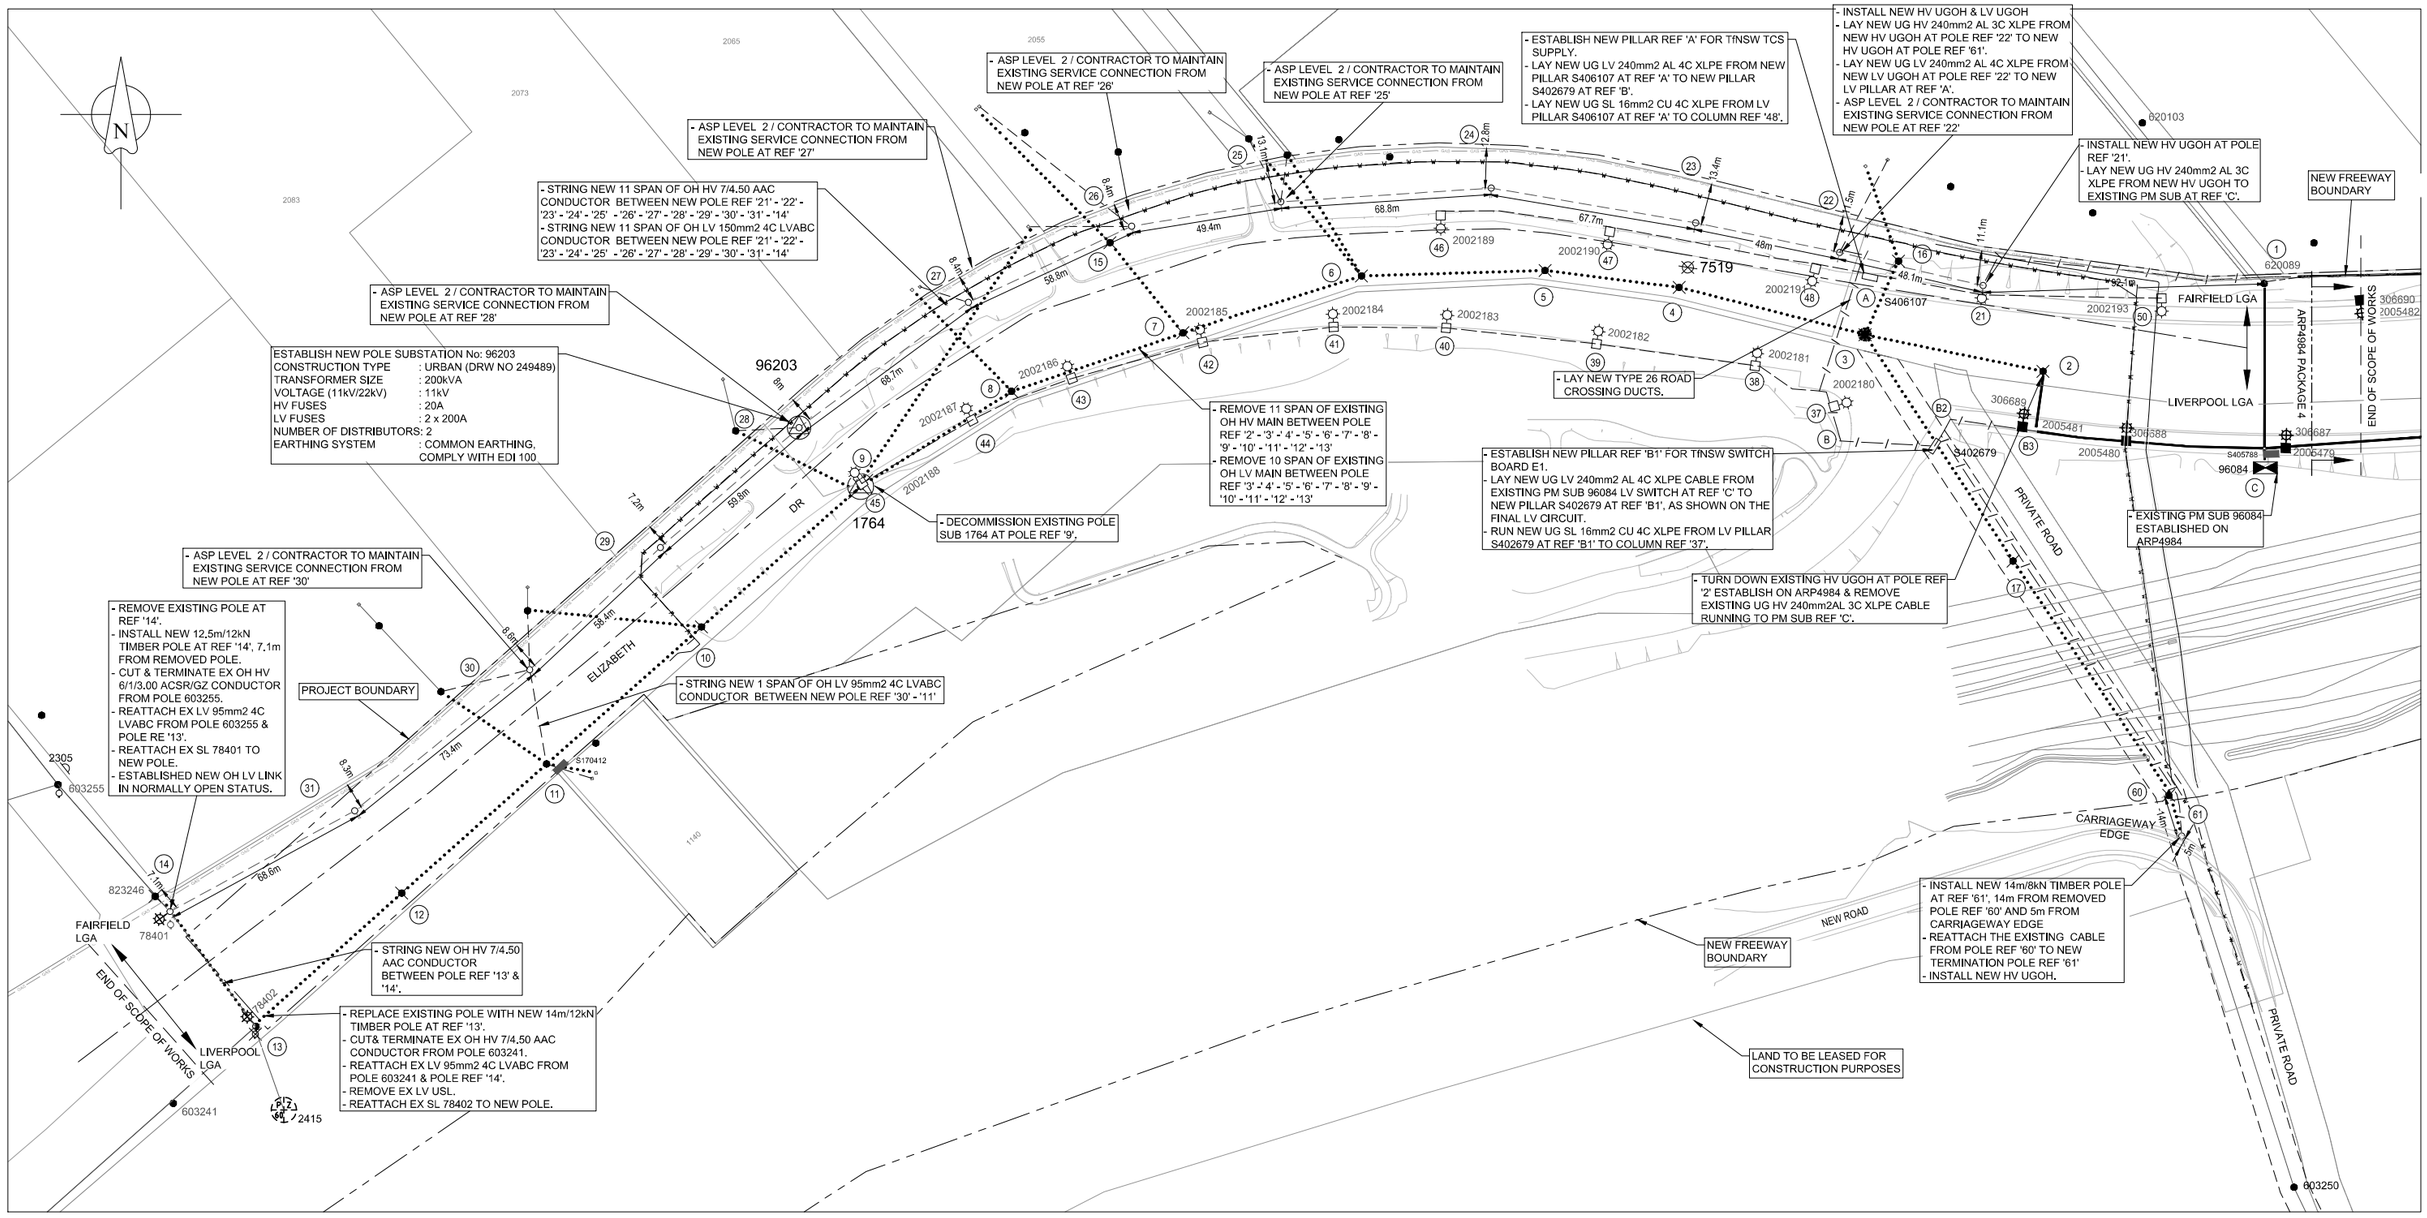

SITE PLAN

0 20 40 60 80 100m

2015 10 5

SCALE 1:1000 @ A1

SITE PLAN LEGEND

- NEW LV TRENCH
- STRING NEW OH CABLE
- EXISTING UNDERGROUND MAINS
- EXISTING OH CABLE
- REMOVE CONDUCTOR
- EXISTING DUCTS
- LGA DEMARCATION
- EXISTING LANTERN
- REMOVE LANTERN
- NEW LANTERN
- EXISTING POLE
- REMOVE POLE
- EXISTING COLUMN
- NEW COLUMN
- EXISTING PILLAR
- PADMOUNT SUBSTATION
- POLE SUBSTATION
- NEW PILLAR
- LV LINK (N/O)
- NEW POLE
- NEW HV TRENCH
- REPLACE POLE
- HV ABS (N/C)
- HV USL (N/C)
- GAS — HIGH PRESSURE GAS
- WATER MAIN
- NEW FREEWAY BOUNDARY
- EXISTING 9,145m WIDTH ENDEAVOUR ENERGY EASEMENT

Cadastre: © Land and Property Information 2016

ASP LEVEL 2 TO RE-ESTABLISH EXISTING SERVICE CONNECTION.

NOTE:
- NEW SL LUMINARIES NUMBER ARE NOT SHOWN ON THE DESIGN FOR CLARITY PURPOSE.

ATTENTION
ALL SERVICES SEARCHES MUST BE CHECKED BEFORE CONSTRUCTION.

BEFORE YOU DIG
www.byda.com.au

CERTIFIED BY ENDEAVOUR ENERGY
Amendment: D
Date Approved: 12-11-2024
Examiner's Signature: Ali Siddiqui
Print Name: Ali Siddiqui
This Certification is issued subject to Endeavour Energy's Standard Certification Terms

WORKS COMPLETED/FIELD BOOK
CONSTRUCTED BY:
WORKS COMPLETED:
SIGNATURE: DATE:
INSPECTED BY:
SIGNATURE: DATE:

ASSET RECORDING
I:
OF:
CONTACT No.:
HEREBY CERTIFY THAT ASSETS MARKED AS-BUILT ON THIS DRAWING HAVE BEEN RECORDED AS PER ENDEAVOR ENERGY STANDARD SAD 0004.
SIGNATURE:
DATE:

AMENDMENTS		
A	ORIGINAL ISSUE	
	DRAFT No. 05	
B	11/03/2024	
	CHK'D	P. P.
	DRWN	D. S.
	MOVE POLE / PILLAR LOCATION AND REPLACED POLE	
C	8/04/2024	
	CHK'D	P. P.
	DRWN	D. S.
	MOVE POLE REF '61' & ESTABLISH STJ AT REF '60'	
D	4/11/2024	
	CHK'D	P. P.
	DRWN	D. S.
	DEMOLISH POLE SUB AT REF 28 & REVISED EARTHING REF 61	

CLIENT:
JOHN HOLLAND M7–M12 Integration Project
NSW GOVERNMENT Transport for NSW

wsp
Level 27, Ernst & Young Centre
680 George Street
Sydney NSW 2000
GPO BOX 5394
Sydney NSW 2001 Australia
Telephone +61 2 9272 5100
Facsimile +61 2 9272 5101
Email sydney@wsp.com
ASP REF/ACCREDIATION NO. - 5045

TEMPLATE VERSION No.5.20

© THIS DRAWING AND THE COPYRIGHT THEREIN IS THE PROPERTY OF ENDEAVOUR ENERGY AND MAY NOT BE COPIED, REPRODUCED, DISTRIBUTED, LOANED OR USED WITHOUT THE WRITTEN CONSENT OF ENDEAVOUR ENERGY

REFERENCE DRAWING'S		WORK ORDERS		CAMS File No.	ARP4983
ULL1937	CONNECTION OF LOAD	GENERAL		AM PROJ. No.	
		OVERHEAD		HV SWITCHING	3284
		UNDERGROUND		EE DEPOT	HOXTON PARK
		SUBSTATIONS		EE REGION	CENTRAL
				HV OP DIAG	KEMPS CREEK 1 D11
				LOCAL GOV AREA	LIVERPOOL

ORIGINAL SCALE

DRAWN	DARSHAN S
DATE	17/07/2023
CH'D	PRAMOD P
DESIGN	DARSHAN S

DO NOT SCALE
DIMENSIONS IN METRES
GDA94/MGA56 COORDINATE SYSTEM

ELIZABETH DRIVE
CECIL PARK
ARP4983
ASSET RELOCATION
M12 EAST - ELIZABETH DRIVE CONNECTION

Endeavour Energy

A1 | 526458 | D

SHEET No 2 OF 9 SHEETS

92119